


LATTO OFFICE

Interior Design


K r a t h u m b a e n , S a m u t s a k h o r n



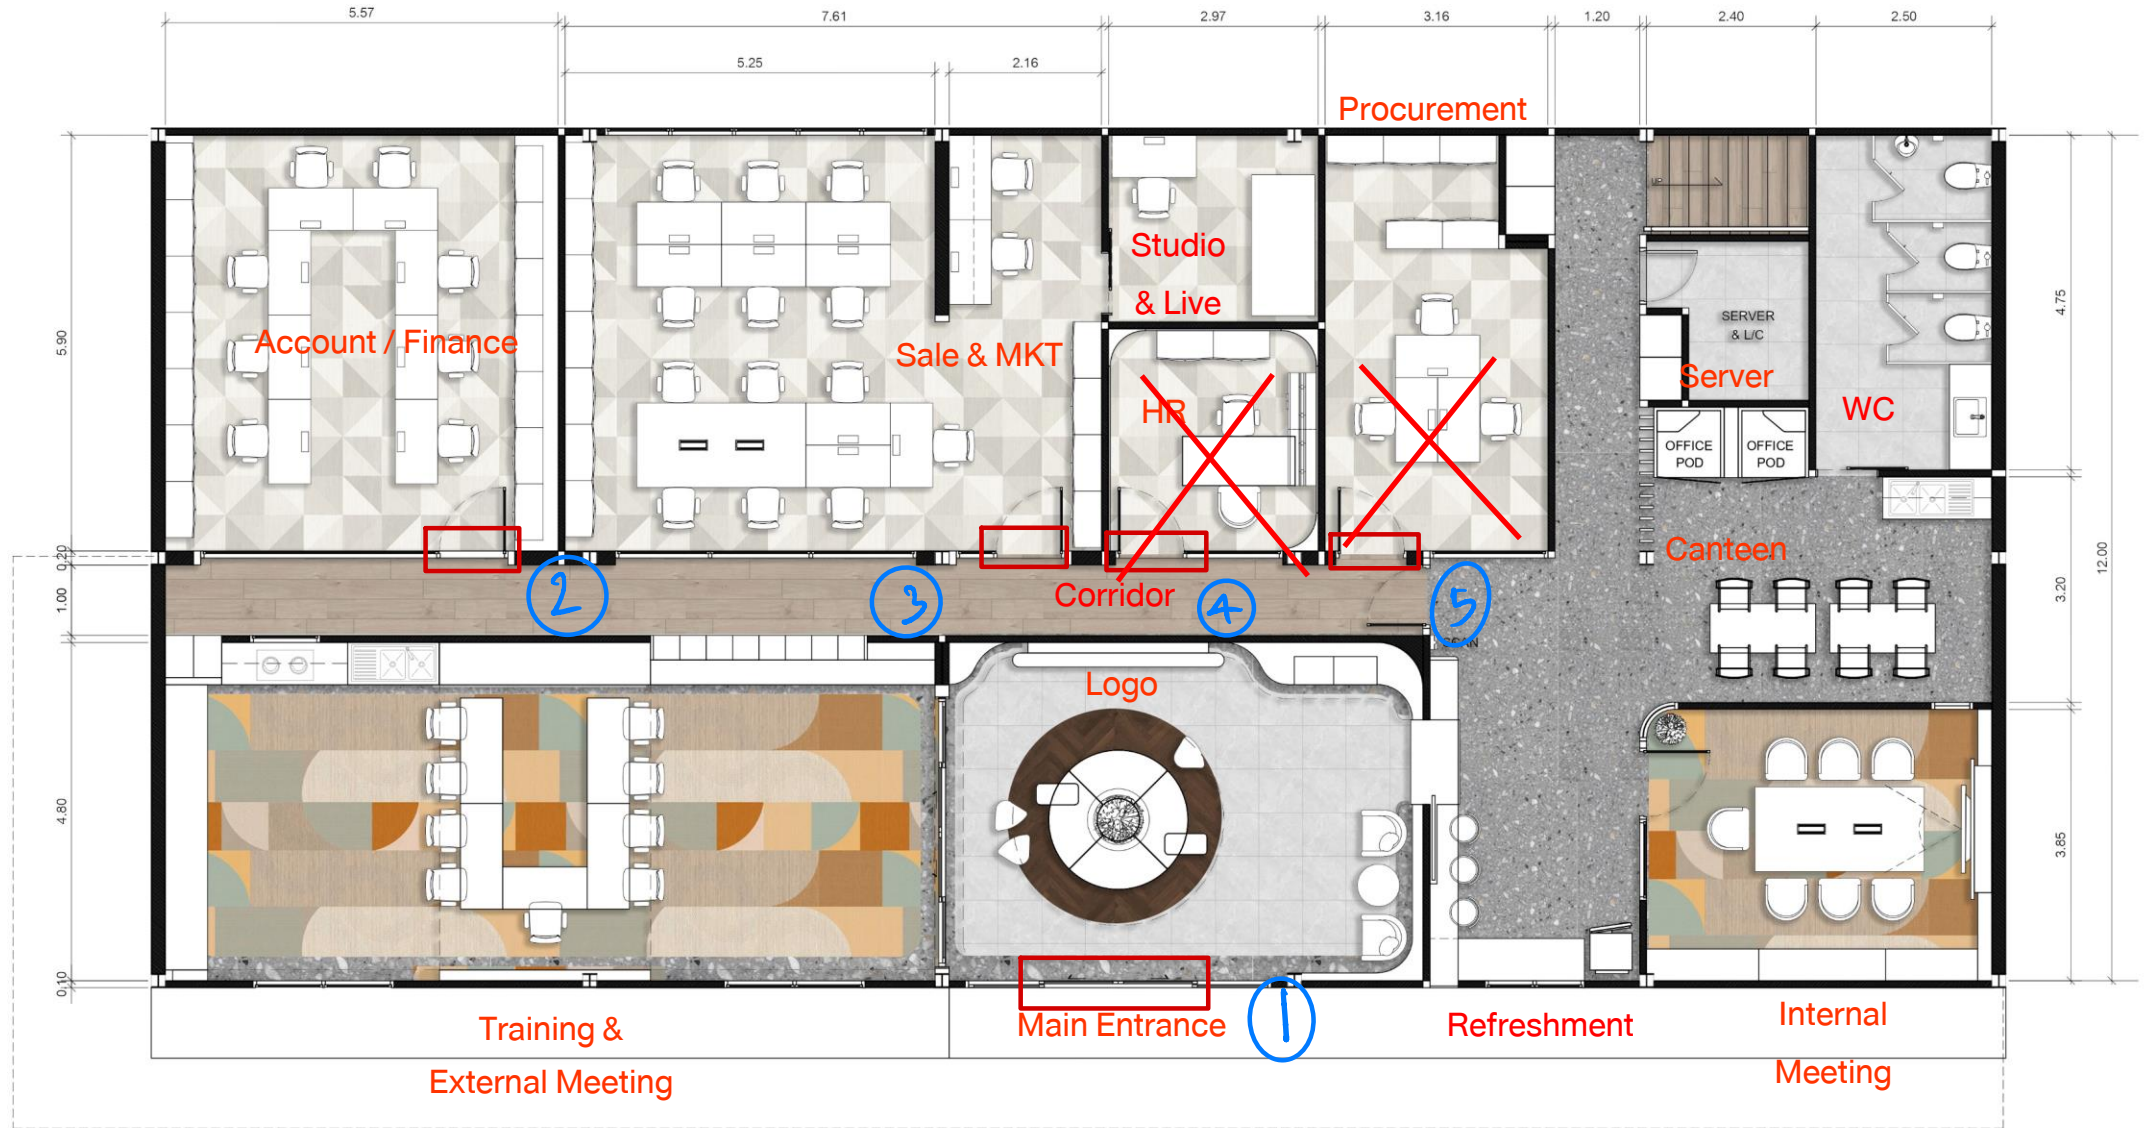

Total 315 SQM.

Office FL. 1st
Layout Plan

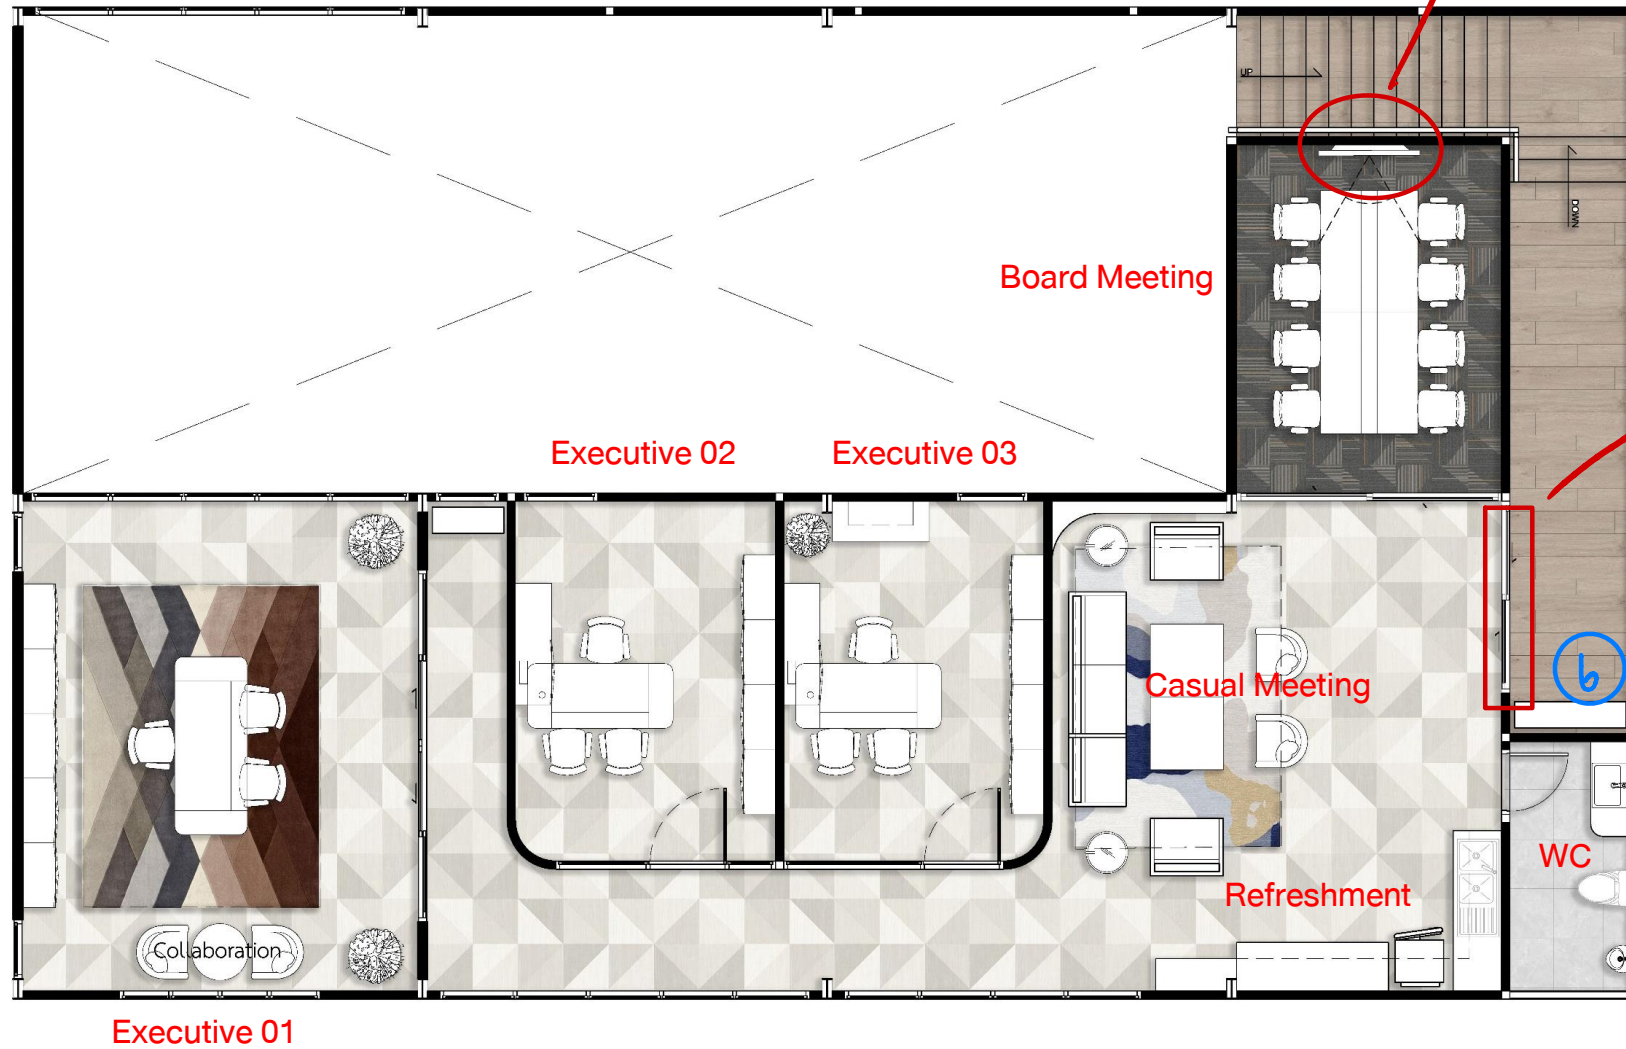

Executive 01

Executive 02

Executive 03

Board Meeting

Casual Meeting

Refreshment

WC

Collaboration

Office FL. 2nd
Layout Plan

Total 120 SQM.

ประตู 1:

เข้า: Face scan+บัตร

ออก: No touch

ประตู 2-6

เข้า: Face scan+บัตร

ออก: No touch

ความต้องการอื่นๆ:



1.กำหนดสิทธิเข้าแต่ละประตู

2.สามารถสั่งเปิดปิดผ่าน app หรือรีโมท



ทางเข้าหลัก

D05

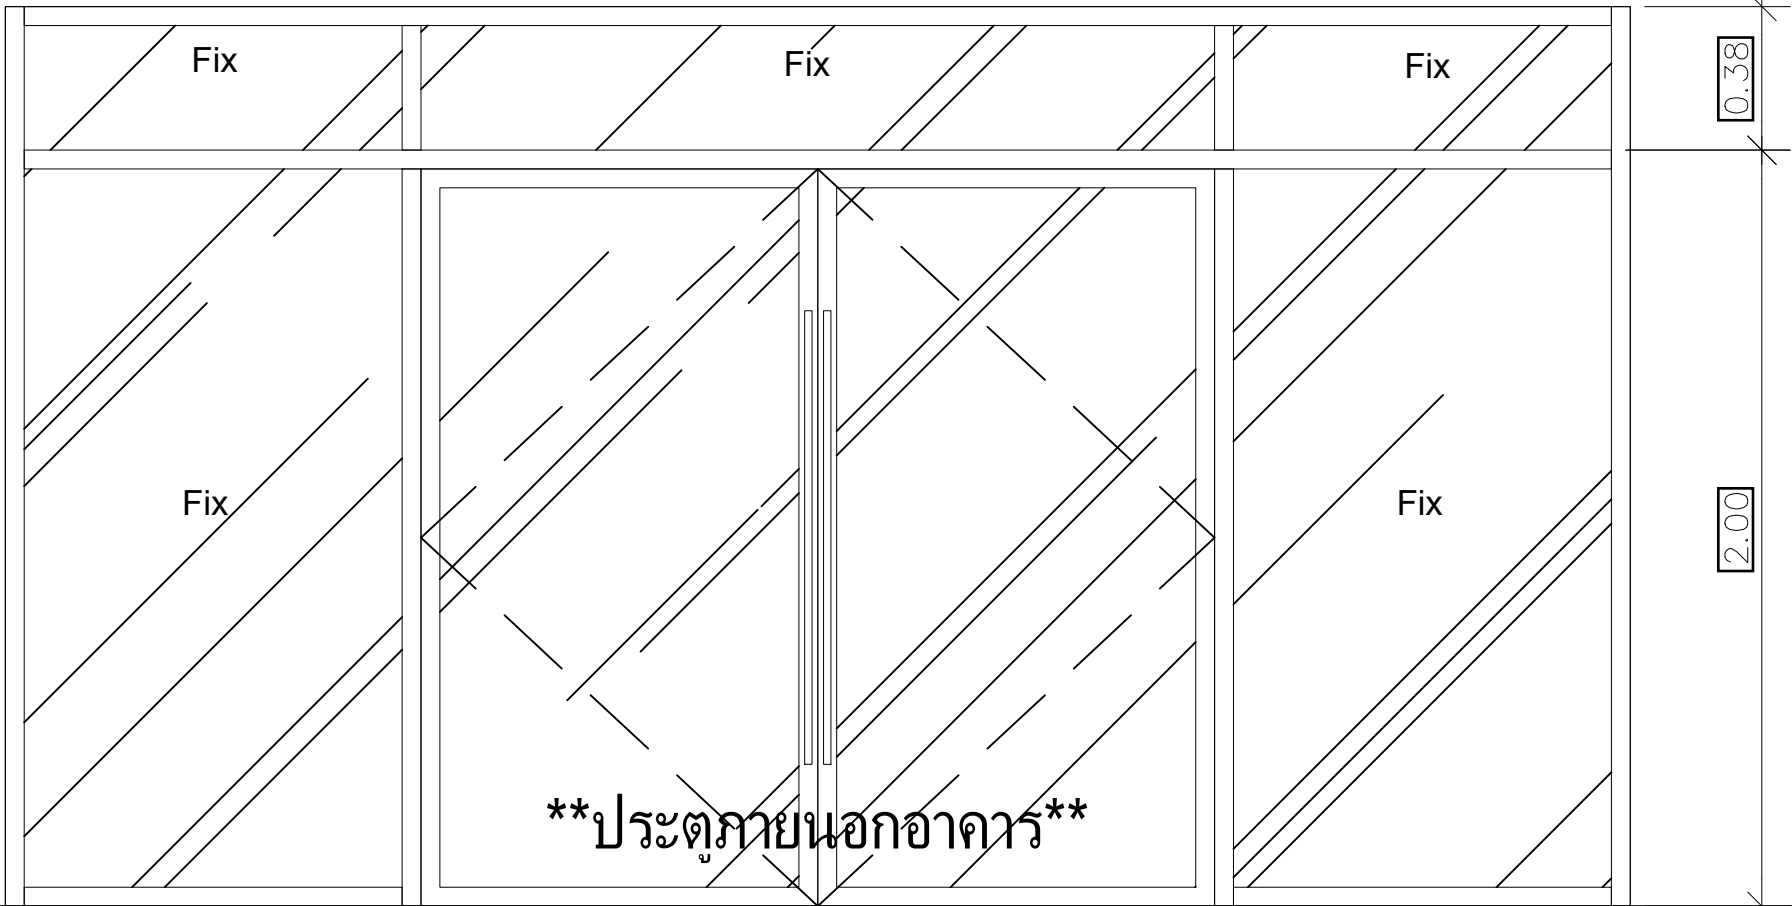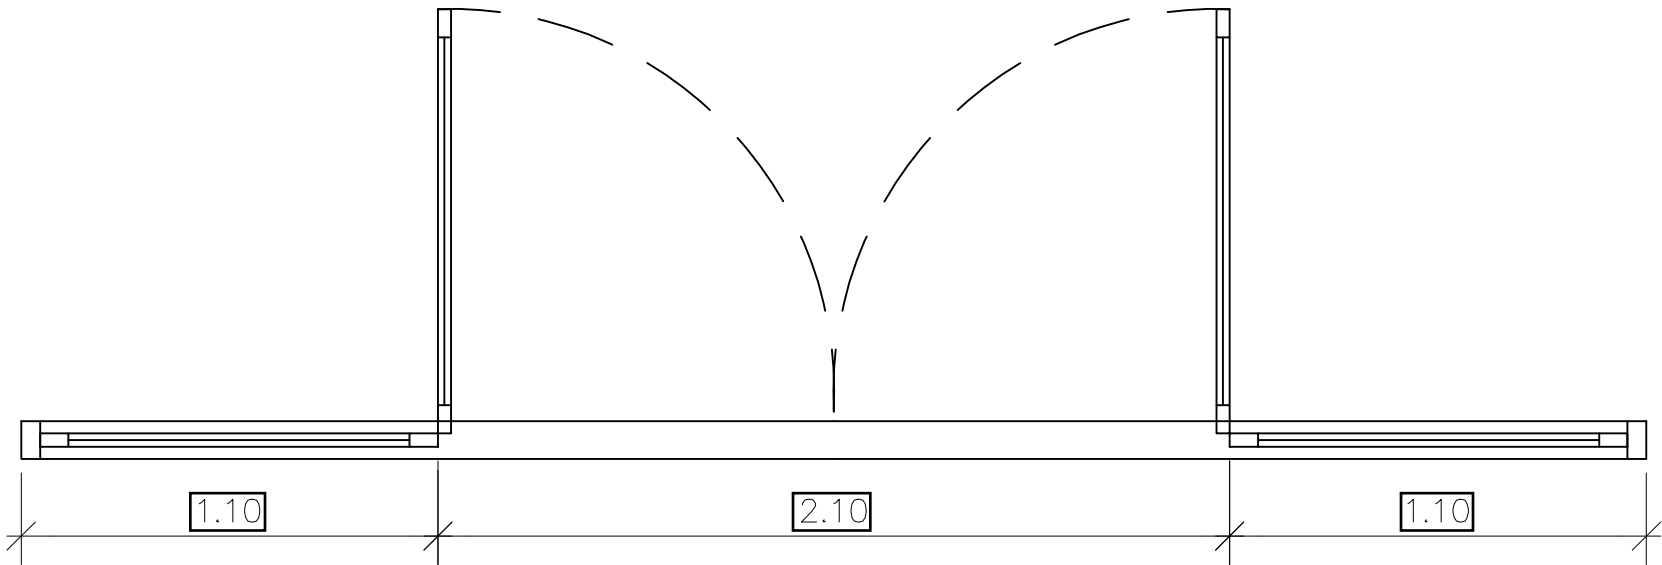

1.10

1.05

1.05

1.10

0.38

2.00


▼ FL+0000

D5

ประตูบานเลื่อนและบานกระຈกติดตาย เฟรมอลูมิเนียม ทางเข้าหลัก

วงกบ	เฟรมอลูมิเนียม Powder coat สี Dark brown ฆ่ารา
กรอบบาน	เฟรมอลูมิเนียม Powder coat สี Dark brown ฆ่ารา
กระຈก	กระຈกโลหะ 8 มม.
มือจับ	มือจับก้านสีดำสูง 1000 มม. พร้อมอุปกรณ์ล็อค
อุปกรณ์	อุปกรณ์รางเลื่อนและล้อค ตามมาตรฐาน

หมายเหตุ	ให้ผู้รับเหมาเช็คขนาดที่หน้างาน ก่อนปฏิบัติงานทุกครั้ง เนื่องจากขนาดจากแบบและหน้างานอาจมีการคลาดเคลื่อน ขนาดอาจไม่ตรงตามแบบให้วัดและตรวจสอบขนาดตามหน้างาน และปรึกษาผู้ออกแบบอีกครั้ง
----------	---

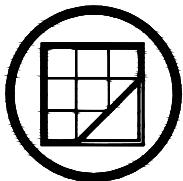

THINK
No.5

THINK NUMBER FIVE Co.,Ltd.

2/34 LADPRAO 101, SOI 38 YAK 1,

KLONG CHAN, BANGKAPI 10240, THAILAND

Email : thinkno.05@gmail.com

GENERAL NOTES

This drawing is the property of Think Number Five Co.,Ltd. and this drawing is a contract. It shall not be used or reproduced without the written permission of Think Number Five Co.,Ltd. All the dimensions are based on figures given. Dimensions shall not be modified from this drawing. The contractor shall be responsible for checking the accuracy of the dimensions and for making any adjustments before starting the work.

Project Name :

LATTO FOOD
OFFICE

Location :

กะทู้แบน
สมุทรสาคร

Owner :

LATTO FOOD & DRINK

Project Director :

Project Designer :

Interior Designer :

Architect :

Landscape Architects :

Structural Engineer :


Civil Engineer :

Electrical Engineer :

Mechanical Engineer :

Sanitary Engineer :

Revise / Issued :

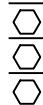

FOR CONSTRUCTION

Project No. :

Drawing Title :

Scale : 1 20

Date : 27/05/2025

Drawn By :

Drawing No. :

Approve By :

ID-D-04

1

In



Out



①




70m09w+LAN

②

บัญชี/การเงิน

D1

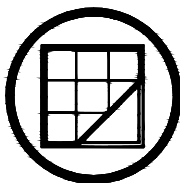

THINK No.5

THINK NUMBER FIVE Co., Ltd.

2/34 LADPRAO 101, SOI 38 YAK 1,

LONG CHAN, BANGKAPI 10240, THA

GENERAL NOTES

These drawings are the property of Think Number Five Co., Ltd and this drawing is a copyright.
 All the dimension are based on figures given.
 Dimensions are not to be scaled from this drawing.
 All the dimension are to be confirmed with the manufacturer of all
 dimensions on site before making any shop drawings
 and before submitting the same.

Project Name :

LATTO FOOD
OFFICE

Location :

กระทู้แบบ
สมทรวสาร

Owner :

LATTO FOOD & DRINK

Project Director :

Project Designer :

Interior Designer :

Architect :

Landscape Architects :

Structural Engineer :


Civil Engineer :

Electrical Engineer :

Mechanical Engineer :

Sanitary Engineer :

Revise / Issued :

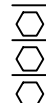

FOR CONSTRUCTION

Project No. :

Drawing Title :

Scale : 1 20

Date : 27/05/2025

Drawn By :

Drawing No. :

Approve By _____

[ID-D-01]

หมายเหตุ	ให้ได้รับเหมาะสมขนาดที่ทำงาน ก่อนปฏิบัติงานทุกครั้ง เนื่องจากขนาดจากแบบและทำงานอาจมีการคลาดเคลื่อน ขนาดอาจไม่ตรงตามแบบให้วัดและตรวจสอบขนาดตามทำงาน และปรึกษาผู้ออกแบบอีกครั้ง
----------	--

D1) ประตูปานเปิด เฟรมอลูมิเนียม ☒ ห้องบัญชีการเงิน

วงกบ	เฟรมอลูมิเนียม Powder coat สี Dark brown ฝ้าอำพัน		
กรอบบาน	เฟรมอลูมิเนียม Powder coat สี Dark brown ฝ้าอำพัน		
กระจก	กระจกใสหนา 8 มม.		
มือจับ	มือจับกันน้ำสีดำสูง 1000 มม. พร้อมอุปกรณ์ล็อค		
อุปกรณ์	อุปกรณ์บานเปิด ตามมาตรฐาน		

▼ FL+0000

②

In




Out





ฝ่ายขาย/การตลาด
D2+W1

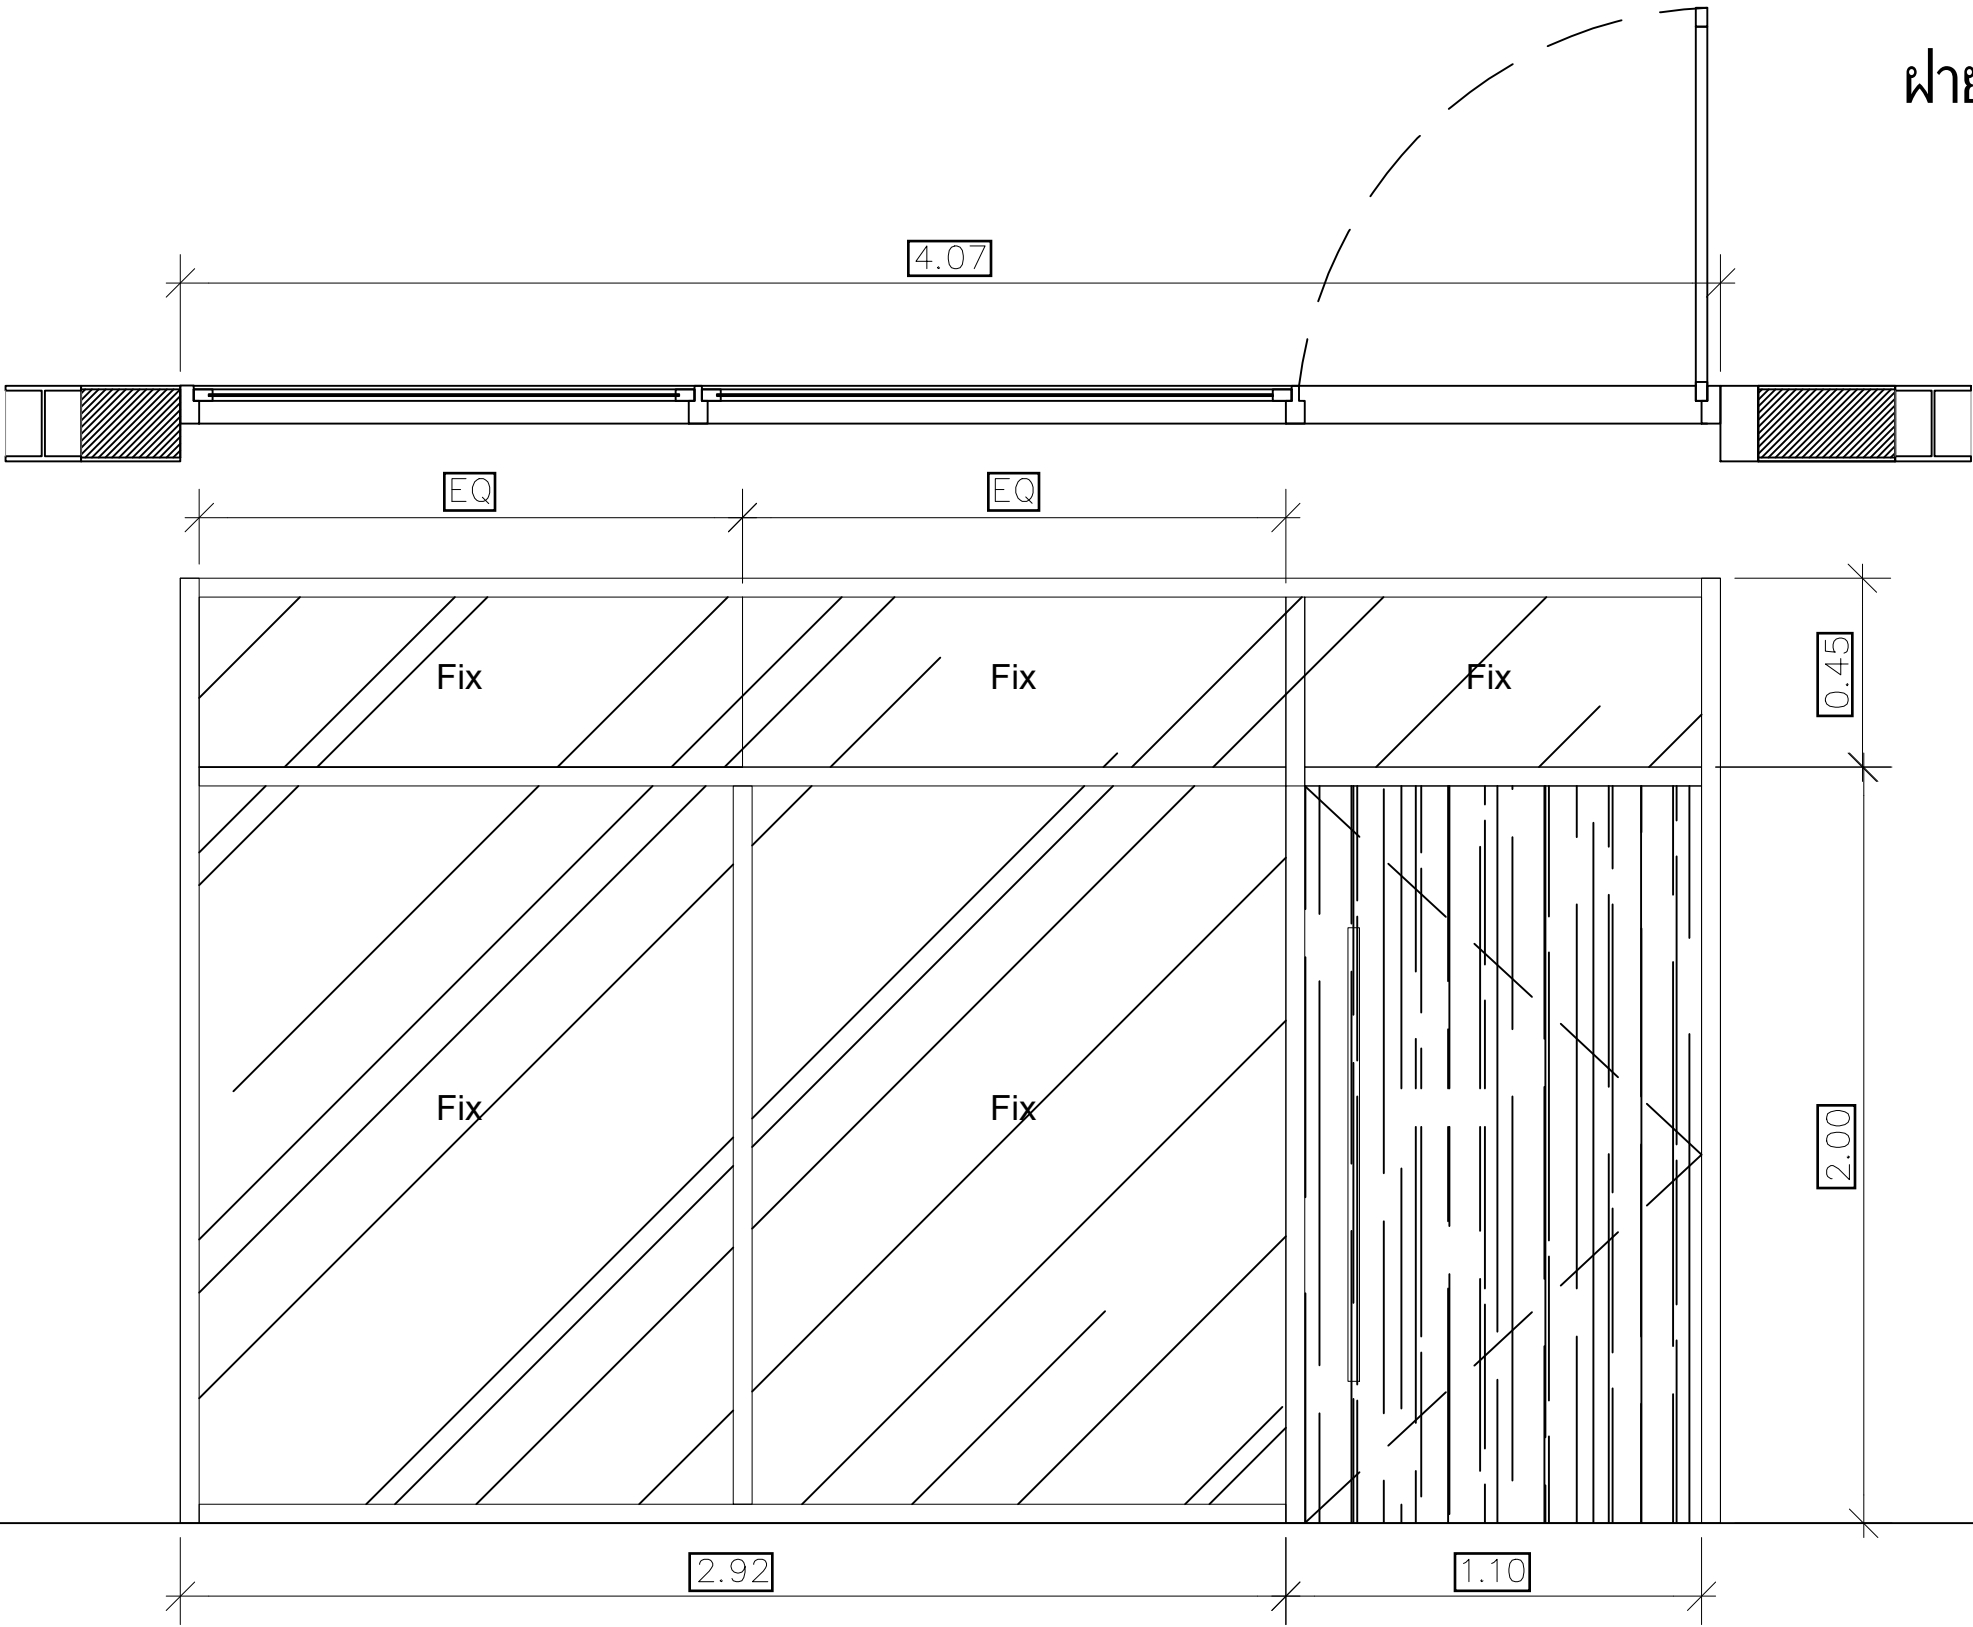


▼ FL+0000

D2 W1 ประตูบานเลื่อนไม้และบานกระจกติดตาย เฟรมอลูมิเนียม / ห้องฝ่ายขายและการตลาด

วงกบ	เฟรมอลูมิเนียม Powder coat สี Dark brown ซ้ำยารั่ว
กรอบบาน	เฟรมอลูมิเนียม Powder coat สี Dark brown ซ้ำยารั่ว
กระจก	กระจกใสหนา 8 มม.
มือจับ	มือจับก้านสีดำสูง 1000 มม. พร้อมอุปกรณ์ล็อค
อุปกรณ์	อุปกรณ์รางเลื่อนและล้อค ตามมาตรฐาน

หมายเหตุ ให้ผู้รับเหมาเช็คขนาดที่หน้างาน ก่อนปฏิบัติงานทุกครั้ง เนื่องจากขนาดจากแบบและหน้างานอาจมีการคลาดเคลื่อน
ขนาดอาจไม่ตรงตามแบบให้วัดและตรวจสอบขนาดตามหน้างาน และปรึกษาผู้ออกแบบอีกครั้ง

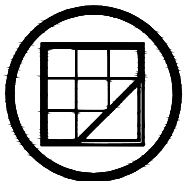

THINK
No.5

THINK NUMBER FIVE Co.,Ltd.

2/34 LADPRAO 101, SOI 38 YAK 1,

KLONG CHAN, BANGKAPI 10240, THAILAND

Email : thinkno.05@gmail.com

GENERAL NOTES

This drawing is the property of Think Number Five Co.,Ltd. and this drawing is a contract.
It shall not be used or reproduced without the written permission of Think Number Five Co.,Ltd.
All the dimensions are based on figures given.
Dimensions shall not be modified from this drawing.
The contractor shall be responsible for any error or omission and shall be liable for any loss or damage caused by the same.

Project Name :

LATTO FOOD
OFFICE

Location :

กระทุ่มแบน
สมุทรสาคร

Owner :

LATTO FOOD & DRINK

Project Director :

Project Designer :

Interior Designer :

Architect :

Landscape Architects :

Structural Engineer :


Civil Engineer :

Electrical Engineer :

Mechanical Engineer :

Sanitary Engineer :

Revise / Issued :

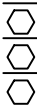

FOR CONSTRUCTION

Project No. :

Drawing Title :

Scale : 1 20

Date : 27/05/2025


Drawn By :





Drawing No. :

Approve By :

ID-D-02

③

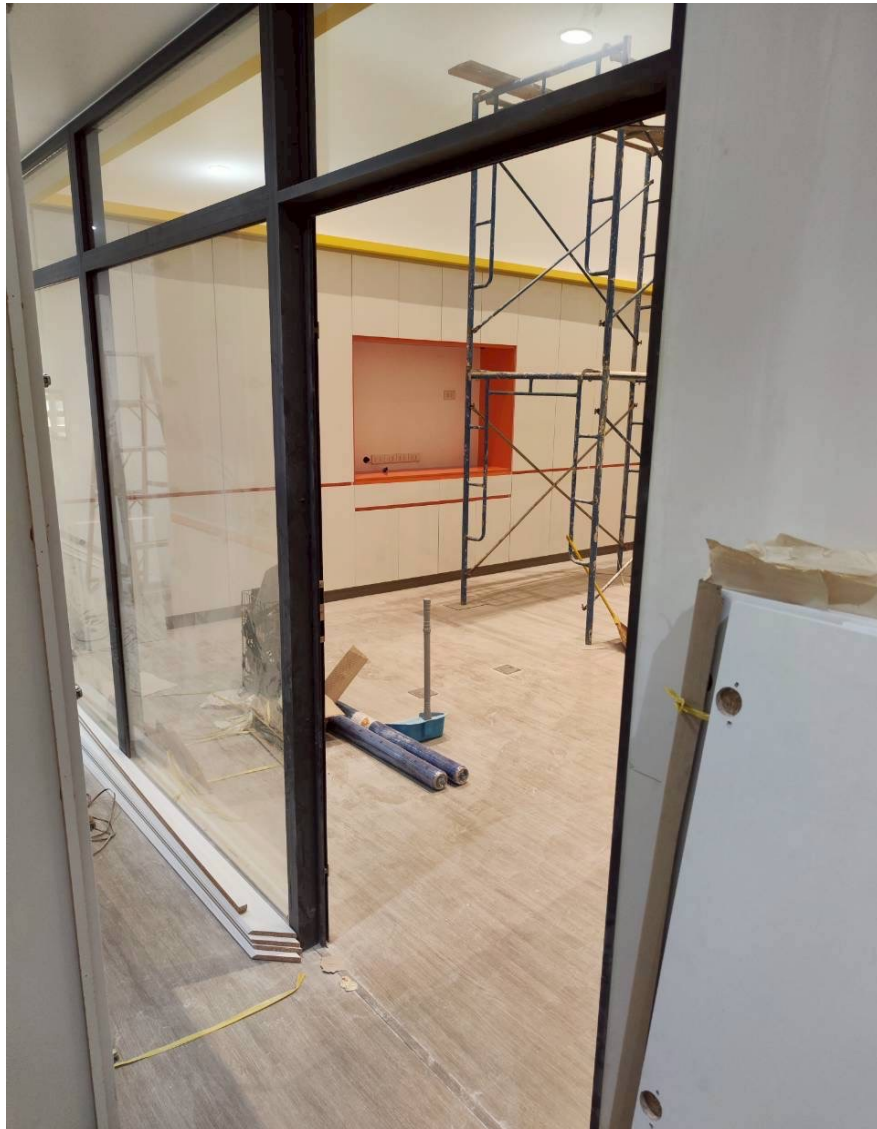

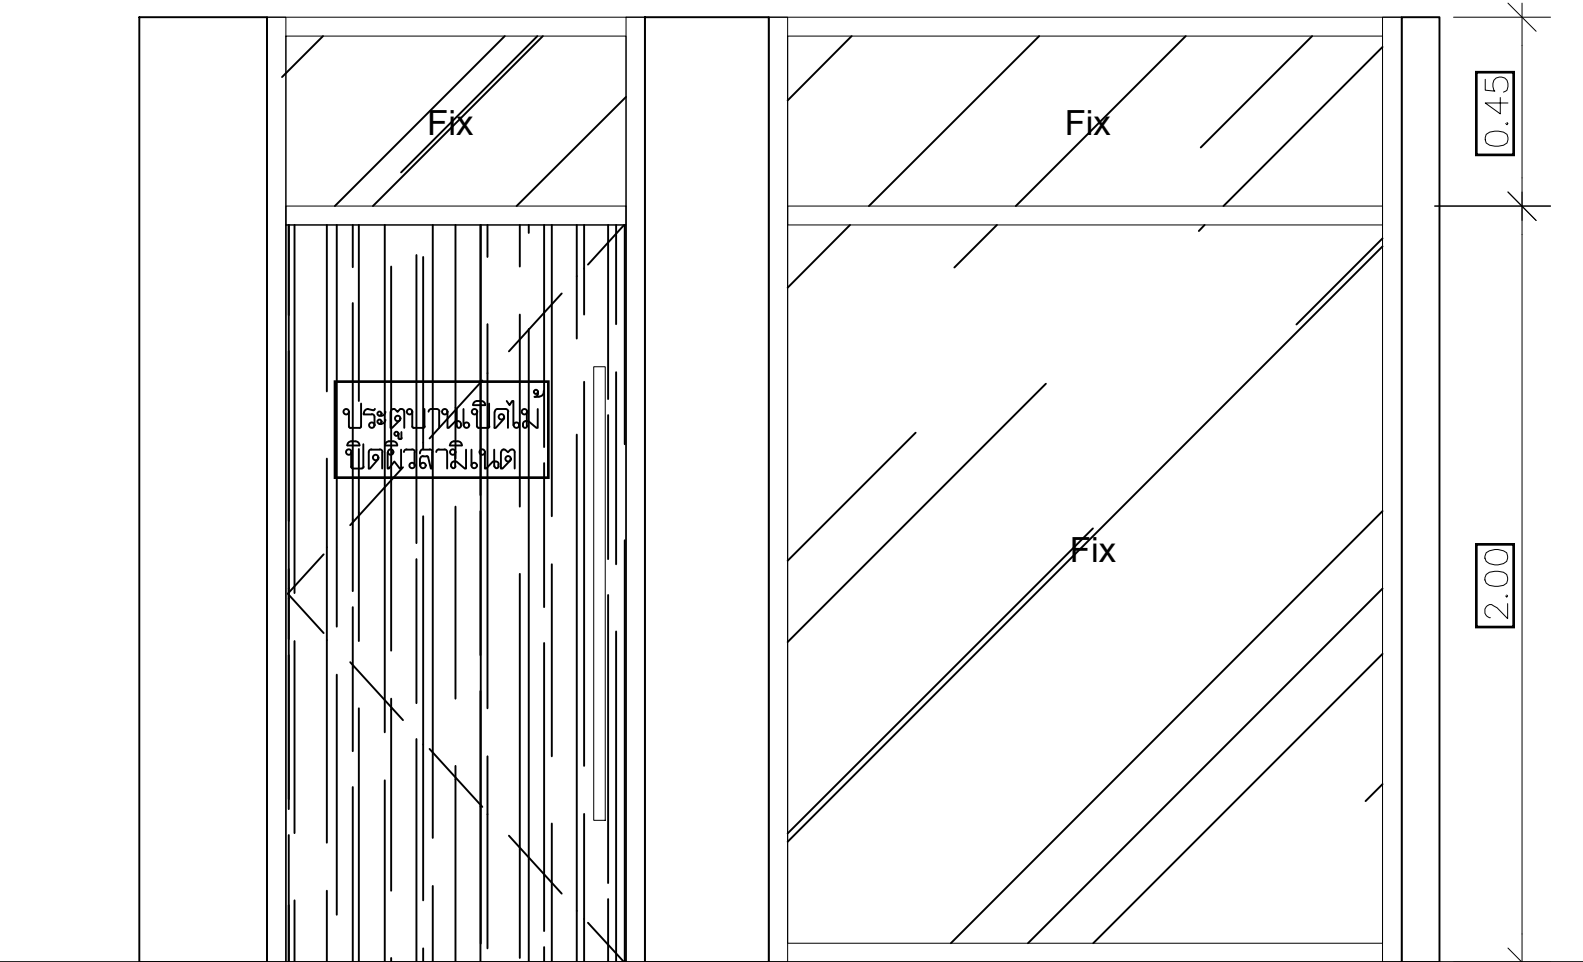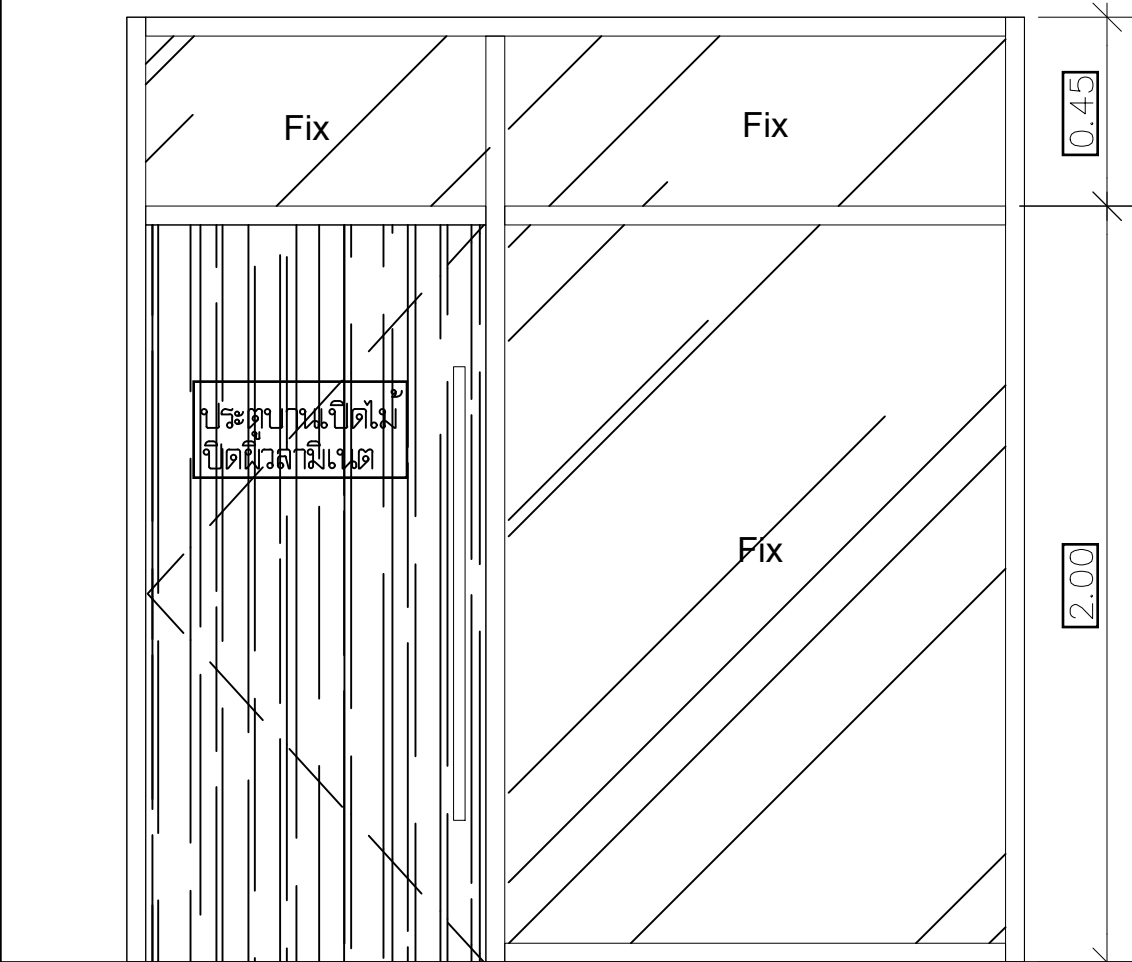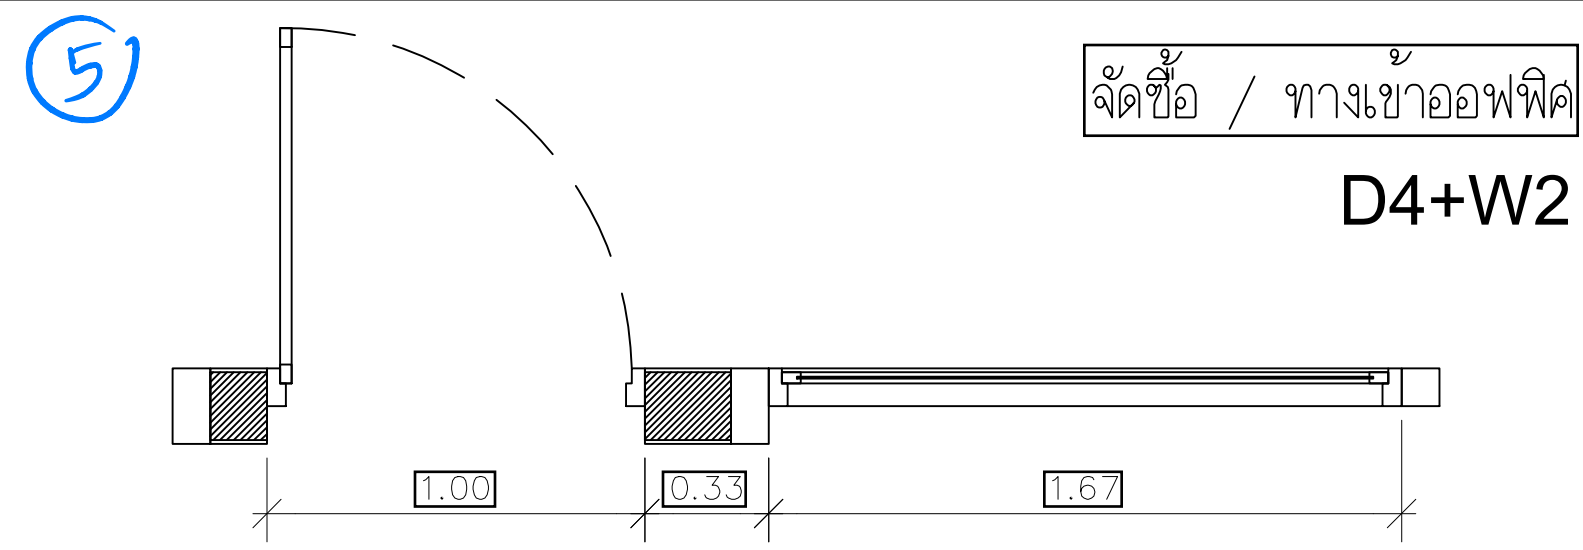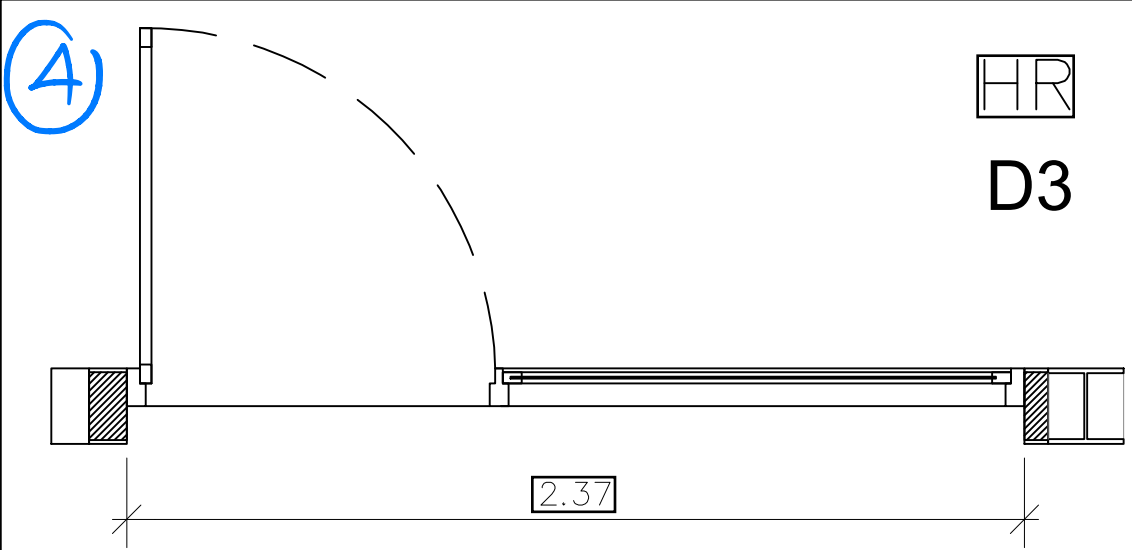

D3 ประตูบานเปิดไม้และบานกระຈกติดตาย เฟรมอลูมิเนียม / ห้อง HR

D4 W2 ประตูบานเปิดไม้และบานกระຈกติดตาย เฟรมอลูมิเนียม / ห้องจัดซื้อ

วงกบ	เฟรมอลูมิเนียม Powder coat สี Dark brown ซ้ำยาร่า
กรอบบาน	เฟรมอลูมิเนียม Powder coat สี Dark brown ซ้ำยาร่า
กระຈก	กระຈกไฉหนา 8 มม.
มือจับ	มือจับก้านสีดำสูง 1000 มม. พร้อมอุปกรณ์ล็อค
อุปกรณ์	อุปกรณ์บานพับ ตามมาตรฐาน

วงกบ	เฟรมอลูมิเนียม Powder coat สี Dark brown ซ้ำยาร่า
กรอบบาน	เฟรมอลูมิเนียม Powder coat สี Dark brown ซ้ำยาร่า
กระຈก	กระຈกไฉหนา 8 มม.
มือจับ	มือจับก้านสีดำสูง 1000 มม. พร้อมอุปกรณ์ล็อค
อุปกรณ์	อุปกรณ์บานพับ ตามมาตรฐาน

THINK No.5

THINK NUMBER FIVE Co., Ltd.

2/34 LADPRAO 101, SOI 38 YAK 1,
KLONG CHAN, BANGKAPI 10240, THAILAND

Email : thinkno.05@gmail.com

GENERAL NOTES

These drawings are the property of Think Number Five Co., Ltd. and this drawing is a contract.

Unauthorized reproduction, modification, or use of this drawing without the written consent of Think Number Five Co., Ltd. is strictly prohibited.

All the dimensions are based on figures given.

Dimensions are not to be modified from this drawing.

Dimensions are not to be modified from this drawing.

Dimensions are not to be modified from this drawing.

Dimensions are not to be modified from this drawing.

Project Name :
LATTO FOOD
OFFICE

Location :
กระทุ่มแบน
สมุทรสาคร

Owner :
LATTO FOOD & DRINK

Project Director :
Project Designer :
Interior Designer :
Architect :
Landscape Architects :
Structural Engineer :
Civil Engineer :
Electrical Engineer :
Mechanical Engineer :
Sanitary Engineer :

Revise / Issued :
○
○
○

FOR CONSTRUCTION

Project No. :
Drawing Title :

Scale : 1 20 Date : 27/05/2025

Drawn By : THIRANANTANA C

Approve By : ID-D-03

หมายเหตุ

ให้รู้รับเหมาเช็คขนาดที่หน้างาน ก่อนปฏิบัติงานทุกครั้ง เนื่องจากขนาดจากแบบและหน้างานอาจมีการคลาดเคลื่อน

ขนาดอาจไม่ตรงตามแบบให้วัดและตรวจสอบขนาดตามหน้างาน และปรึกษาผู้ออกแบบอีกครั้ง

หมายเหตุ	ให้ได้รับเหมาเหมาขนาดที่พนักงาน ก่อนปฏิบัติงานทุกครั้ง เนื่องจากขนาดจากแบบและพนักงานอาจมีการคลาดเคลื่อน ขนาดอาจไม่ตรงตามแบบให้วัดและตรวจสอบขนาดตามพนักงาน และปรึกษาผู้ออกแบบอีกครั้ง
----------	--

6

